Région Souss Massa Province de Agadir Idaoutanane Commune Agadir Ben Serga, Hay Amzil Pté dite: Riad Amzil 44

Plan de Relevé de l'existant du Villa semi fini objet du T194148/09

Référence Fonciers :	Contenance:	Echelle : 1/100	Date : 20/12/2024
T.194148/09	2 <sup>a</sup> 16 <sup>ca</sup>	Num plan : 1/1	<i>Réf Dos : 22-DN454</i>
Leve par : A.O	DAO : A.O	Vérifie par : A.O	Num Fichier : E.L




## BUREAU DES ETUDES TECHNIQUES D'INGENIERIE ET TRAVAUX TOPOGRAPHIQUES SARL E-mail : ingtratop@gmail.com


E-mail : Ingtratop@gmail.com
Tél : +212528 82 74 91 Fax: 212528 82 71 06 QI PLACE DES TAXIS IMM O.E.S N°6 AGADIR

Situation sur Image Satellite



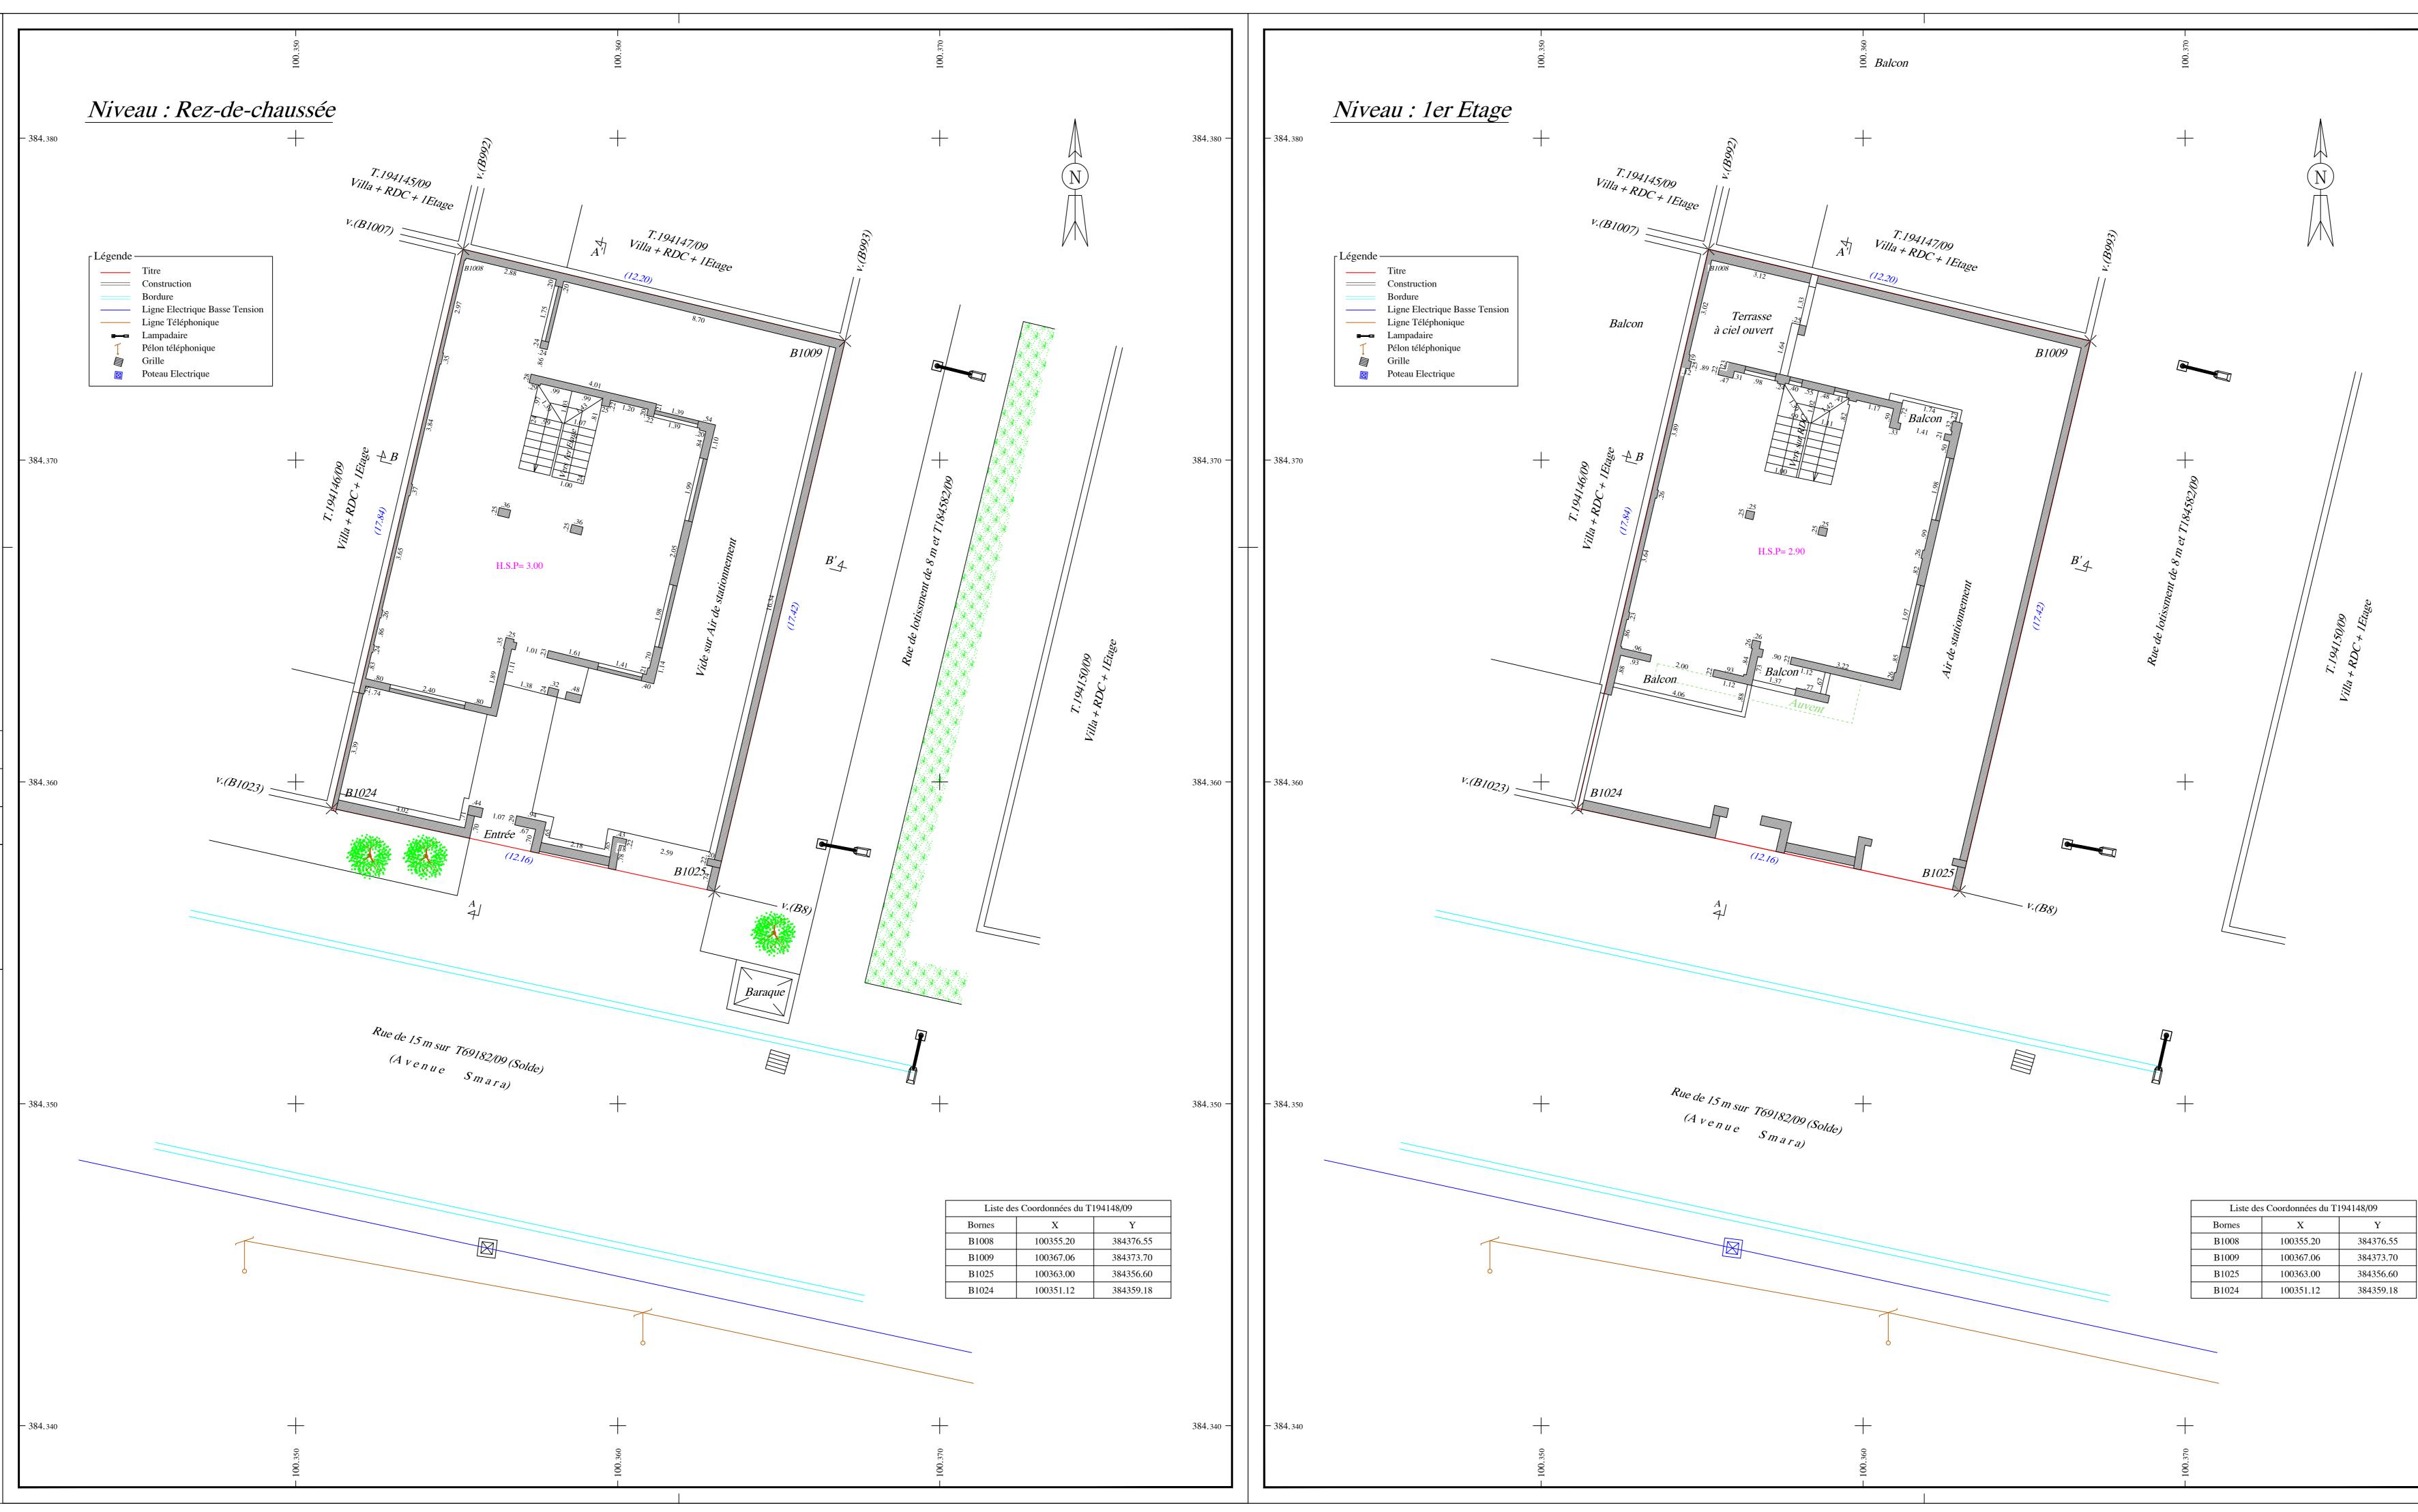

## Niveau : Coupe AA'

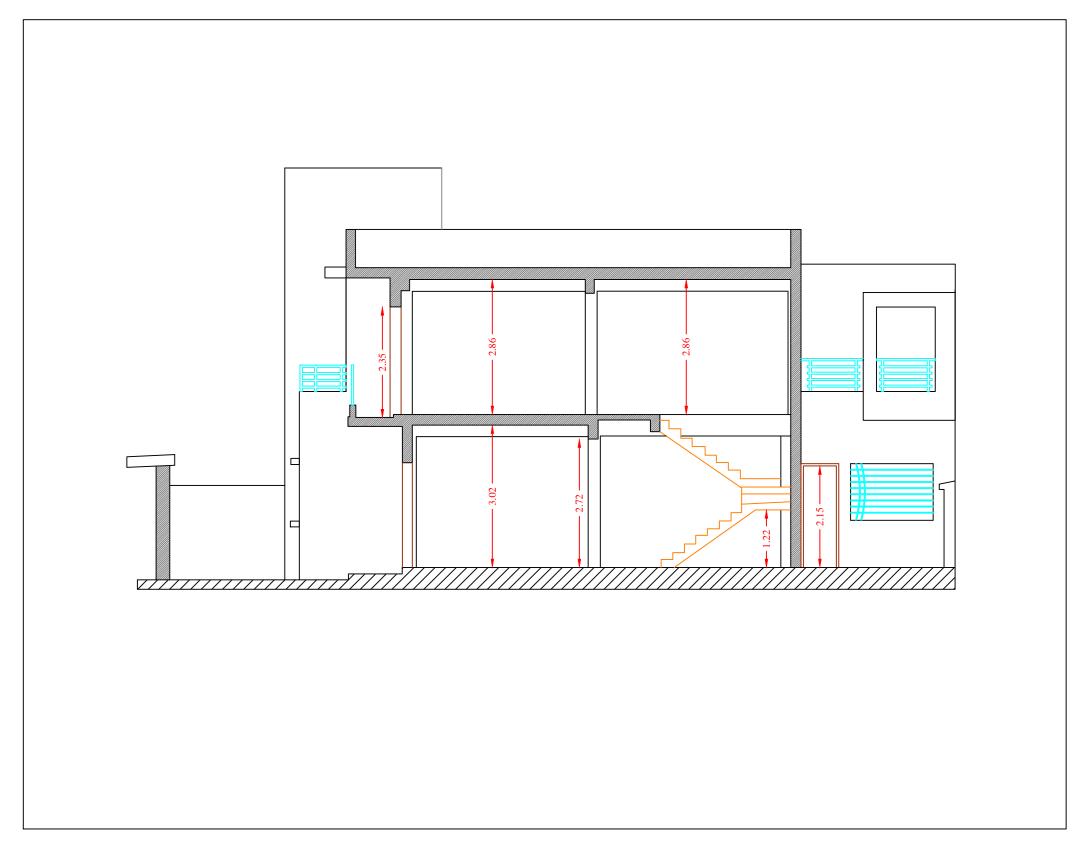

## Niveau : Coupe BB'

